

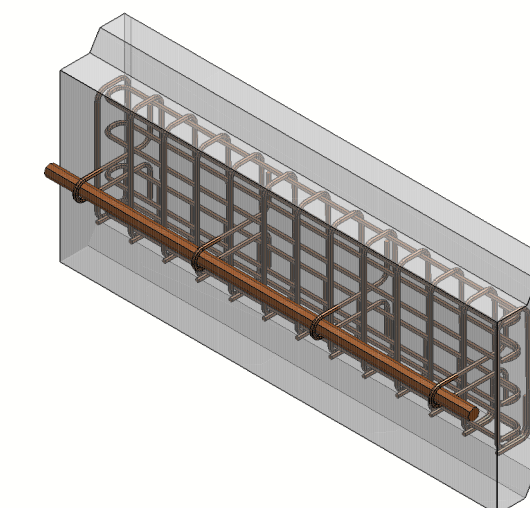
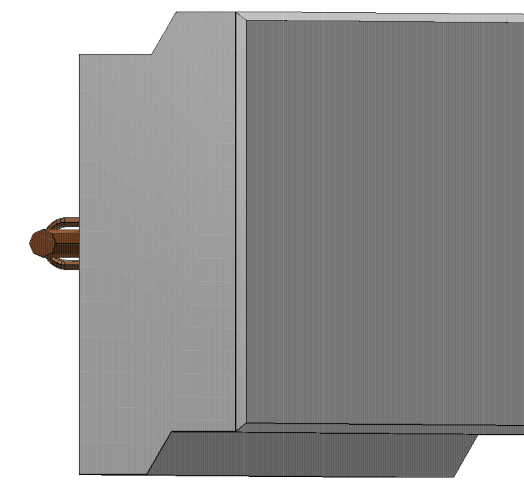
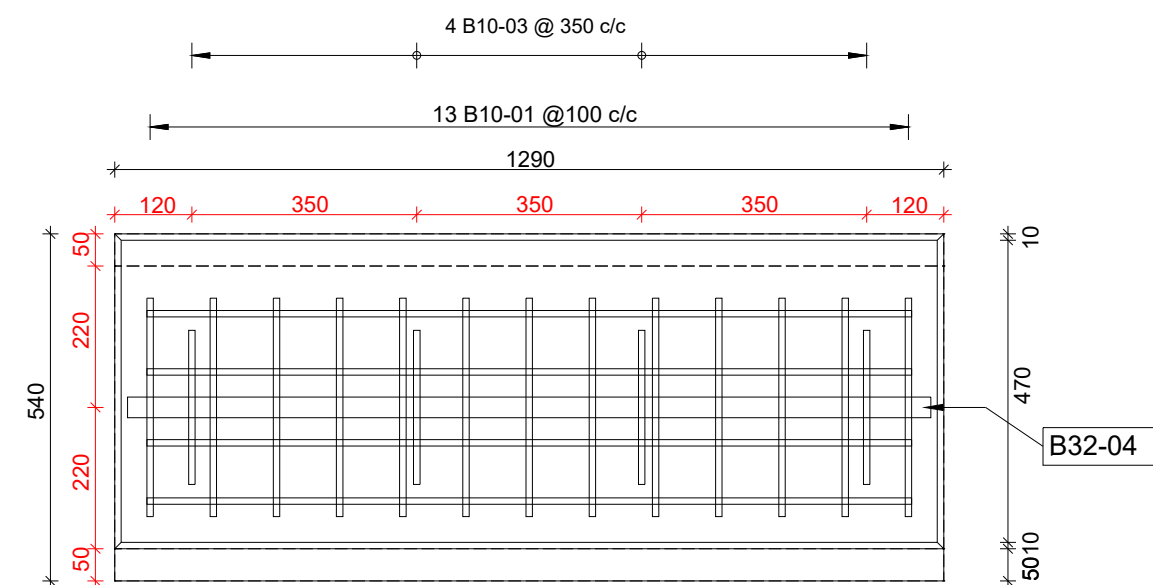
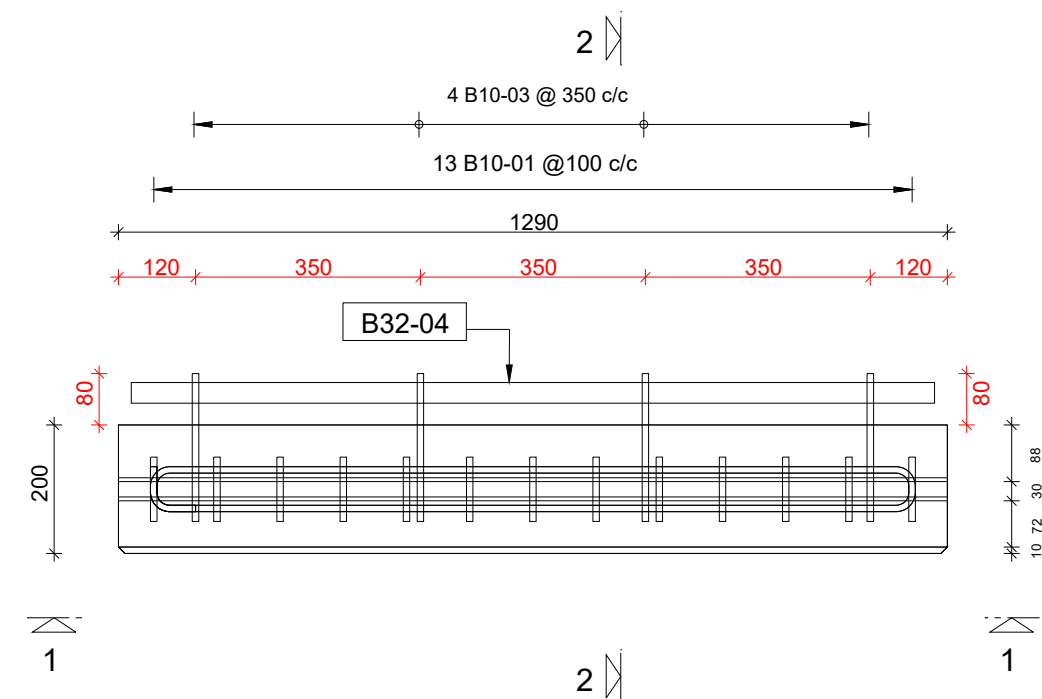



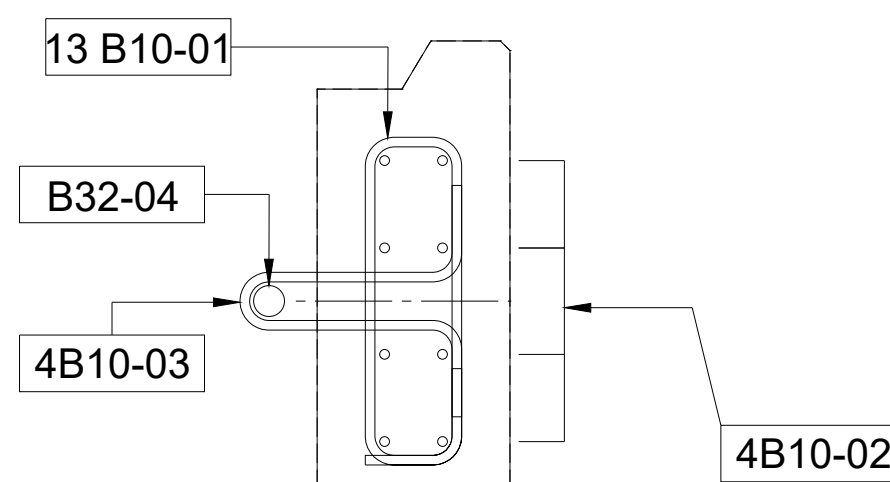


3D VIEW
DRAWN NOT TO SCALE

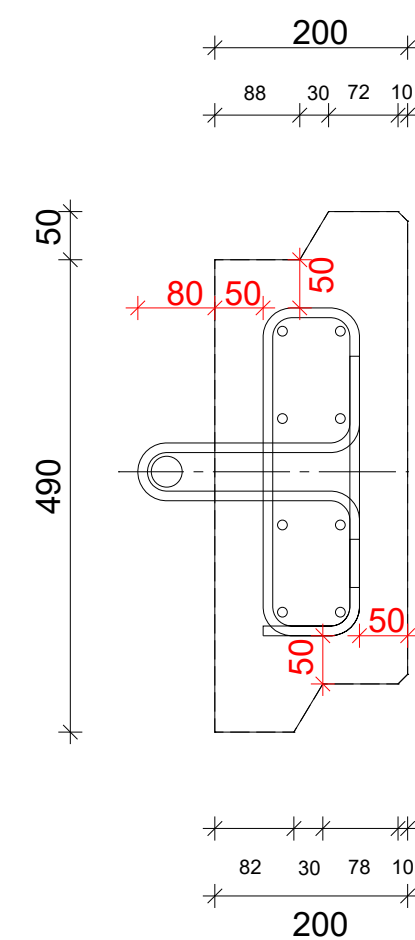




SECTION 2 - 2


REBAR DETAILS

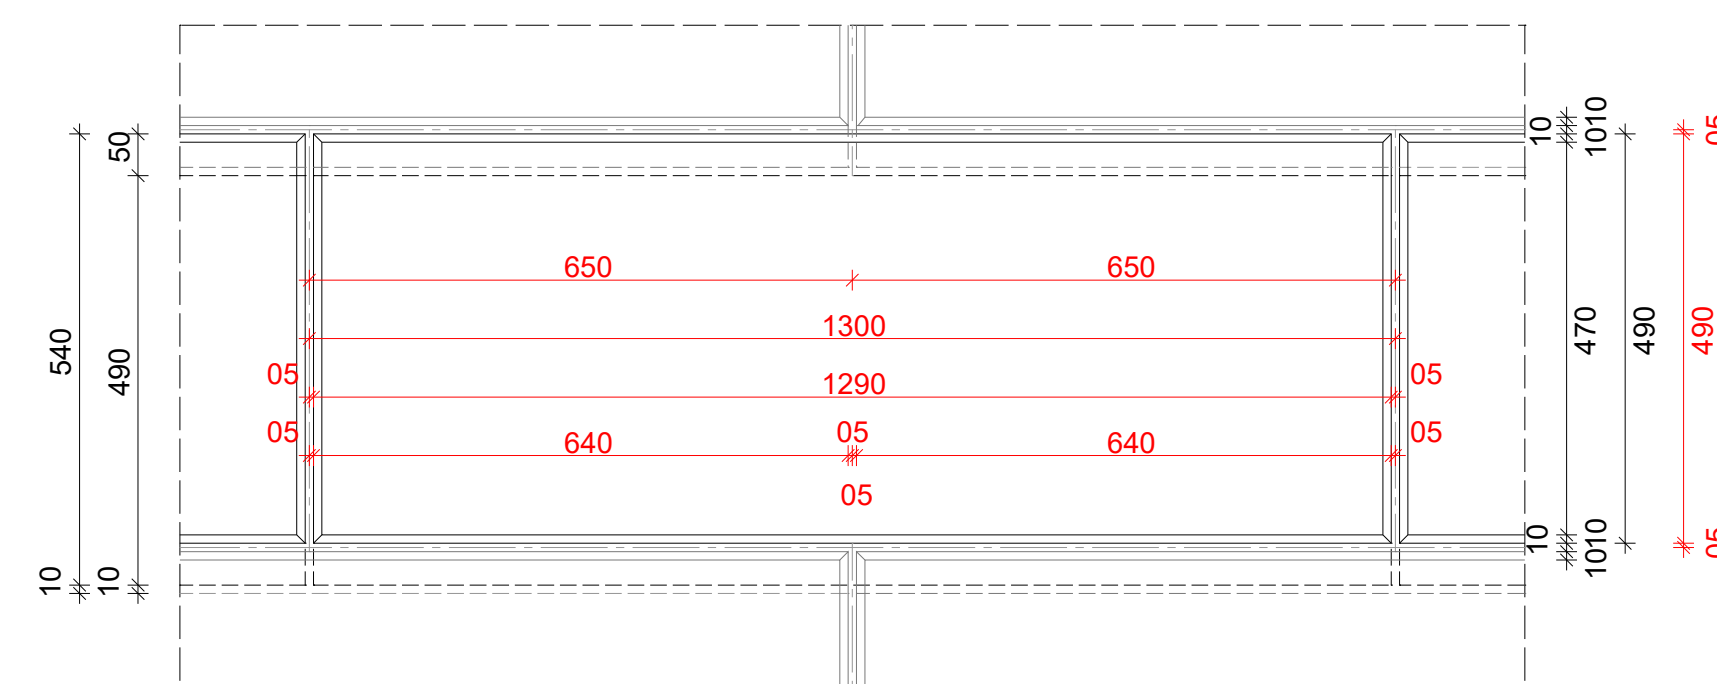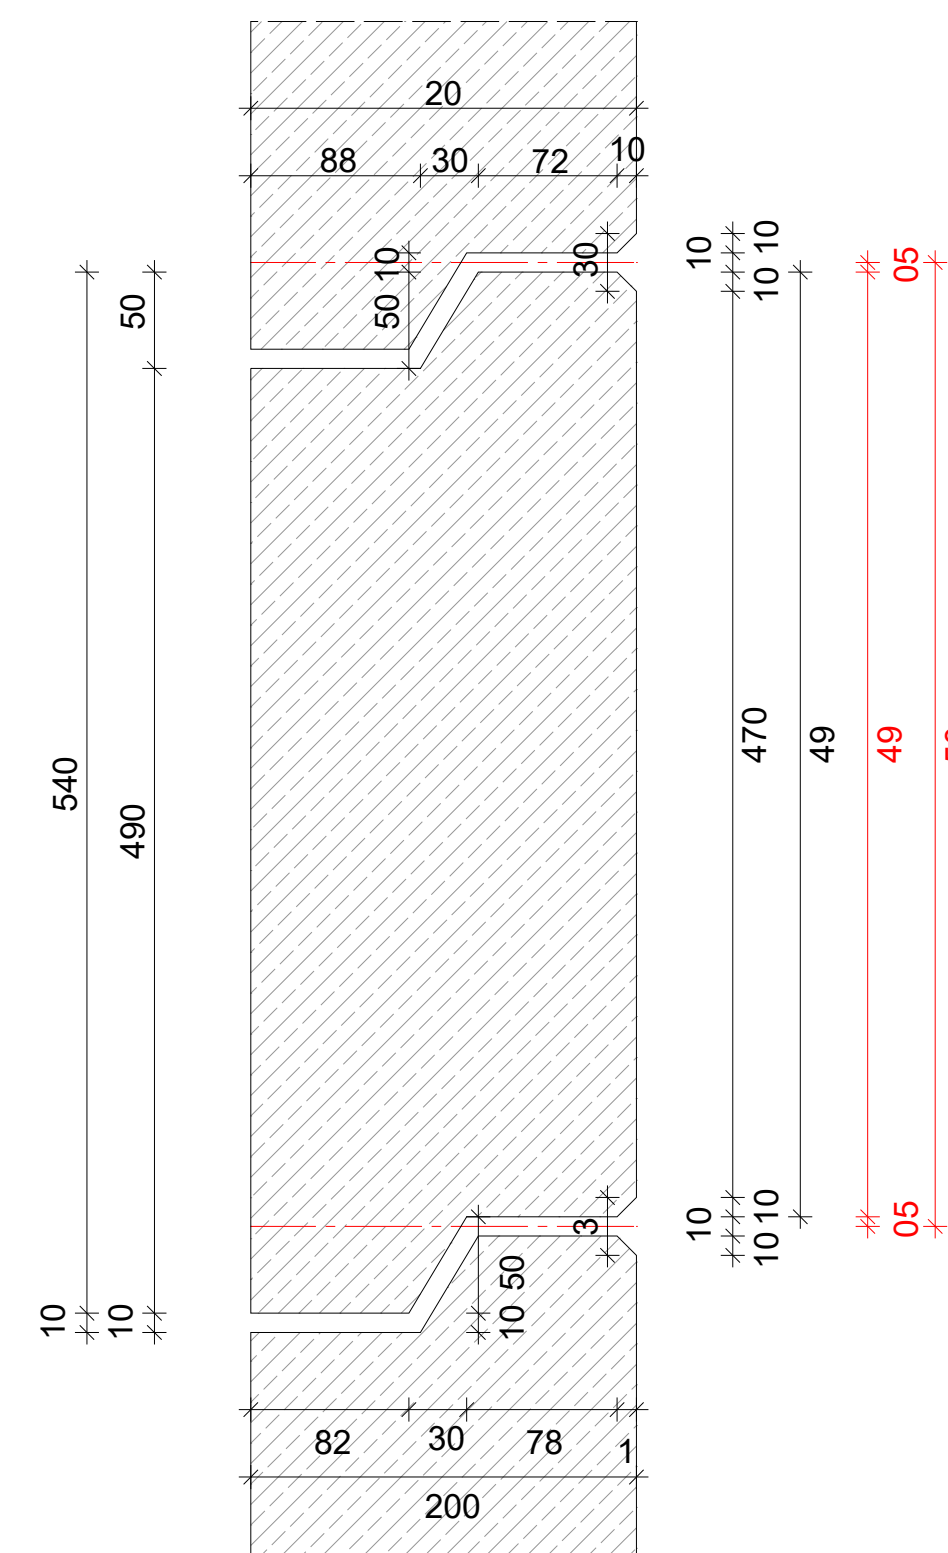

DETAIL A
FRONT VIEW

BENDING SCHEDULE

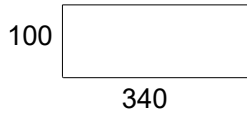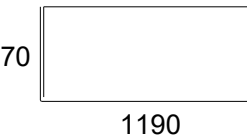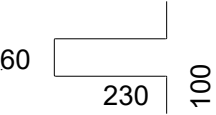member	bar mark	type & size (mm)	No. of mbrs	No. in each	total No.	length of each bar (mm)	shape
Panel	01	B10		13		980	
Panel	02	B10		4		2590	
Panel	03	B10		4		720	
Panel	04	B32		1		1250	

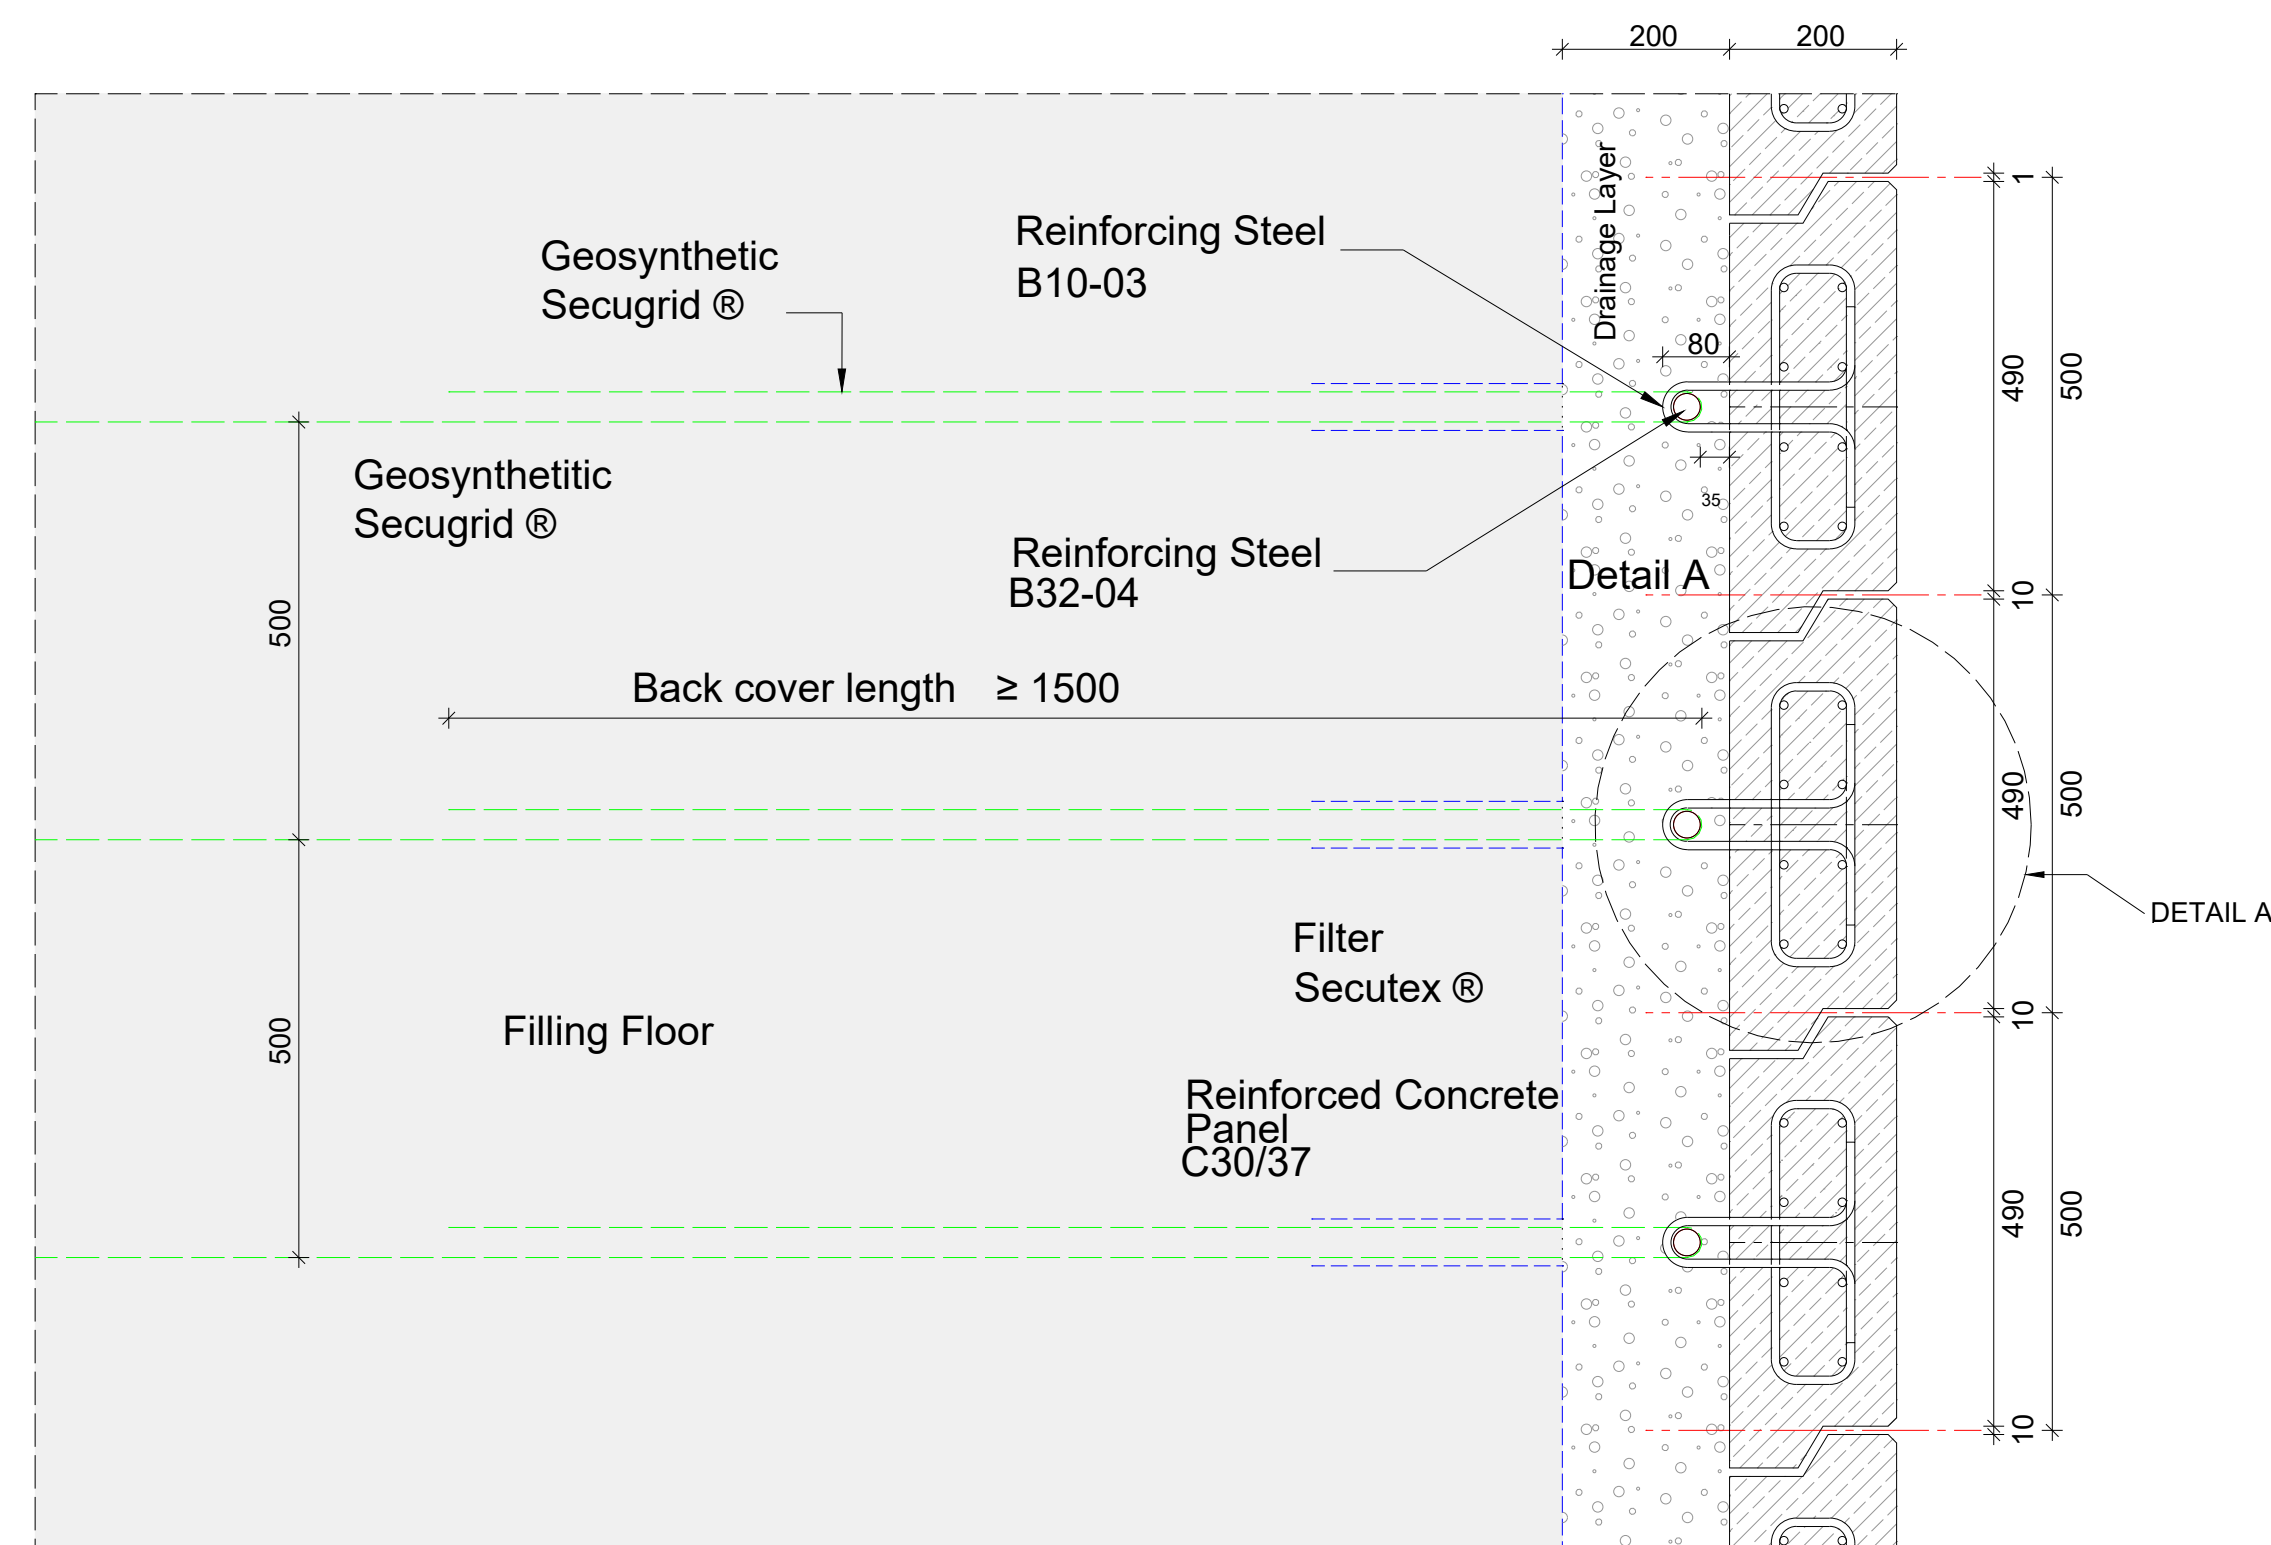


DETAIL A SIDE VIEW

- 1). THIS DRAWING IS TO BE READ IN CONJUNCTION WITH ALL OTHER RELEVANT DRAWINGS, ANY DISCREPANCIES, ERRORS OR OMISSIONS TO BE BROUGHT TO THE ATTENTION OF CPLEX COMPANY LTD-ENG DIV.
- 2). ALL DIMENSIONS TO BE CHECKED BEFORE COMMENCEMENT OF WORK ON SITE.

P01 WGK IFM	DISCUSSION	09/02/24 ST
REV. DRN. CKD	COMMENTS	DATE APD

KEY TO HEALTH & SAFETY SYMBOLS:

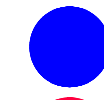

GOVERNMENT OF THE REPUBLIC OF GHANA
MINISTRY OF ROADS AND HIGHWAYS
GHANA HIGHWAY AUTHORITY

Project:	KASOA -WINNEBA
----------	----------------

Drawing:	GEOGRID REINFORCED CONCRETE PANEL DETAILS
----------	--

Purpose of issue:	PRELIMINARY
-------------------	-------------

Client Project Number:	Sc
------------------------	----

— 100 —

DO NOT SCALE FROM
DRAWING

Drawing Number:
CP24-KW-AWE

Status:	
---------	--

Drawing Sheet Size:

	A1
Sheet Number:	1 of 1

Rev.:
P01