


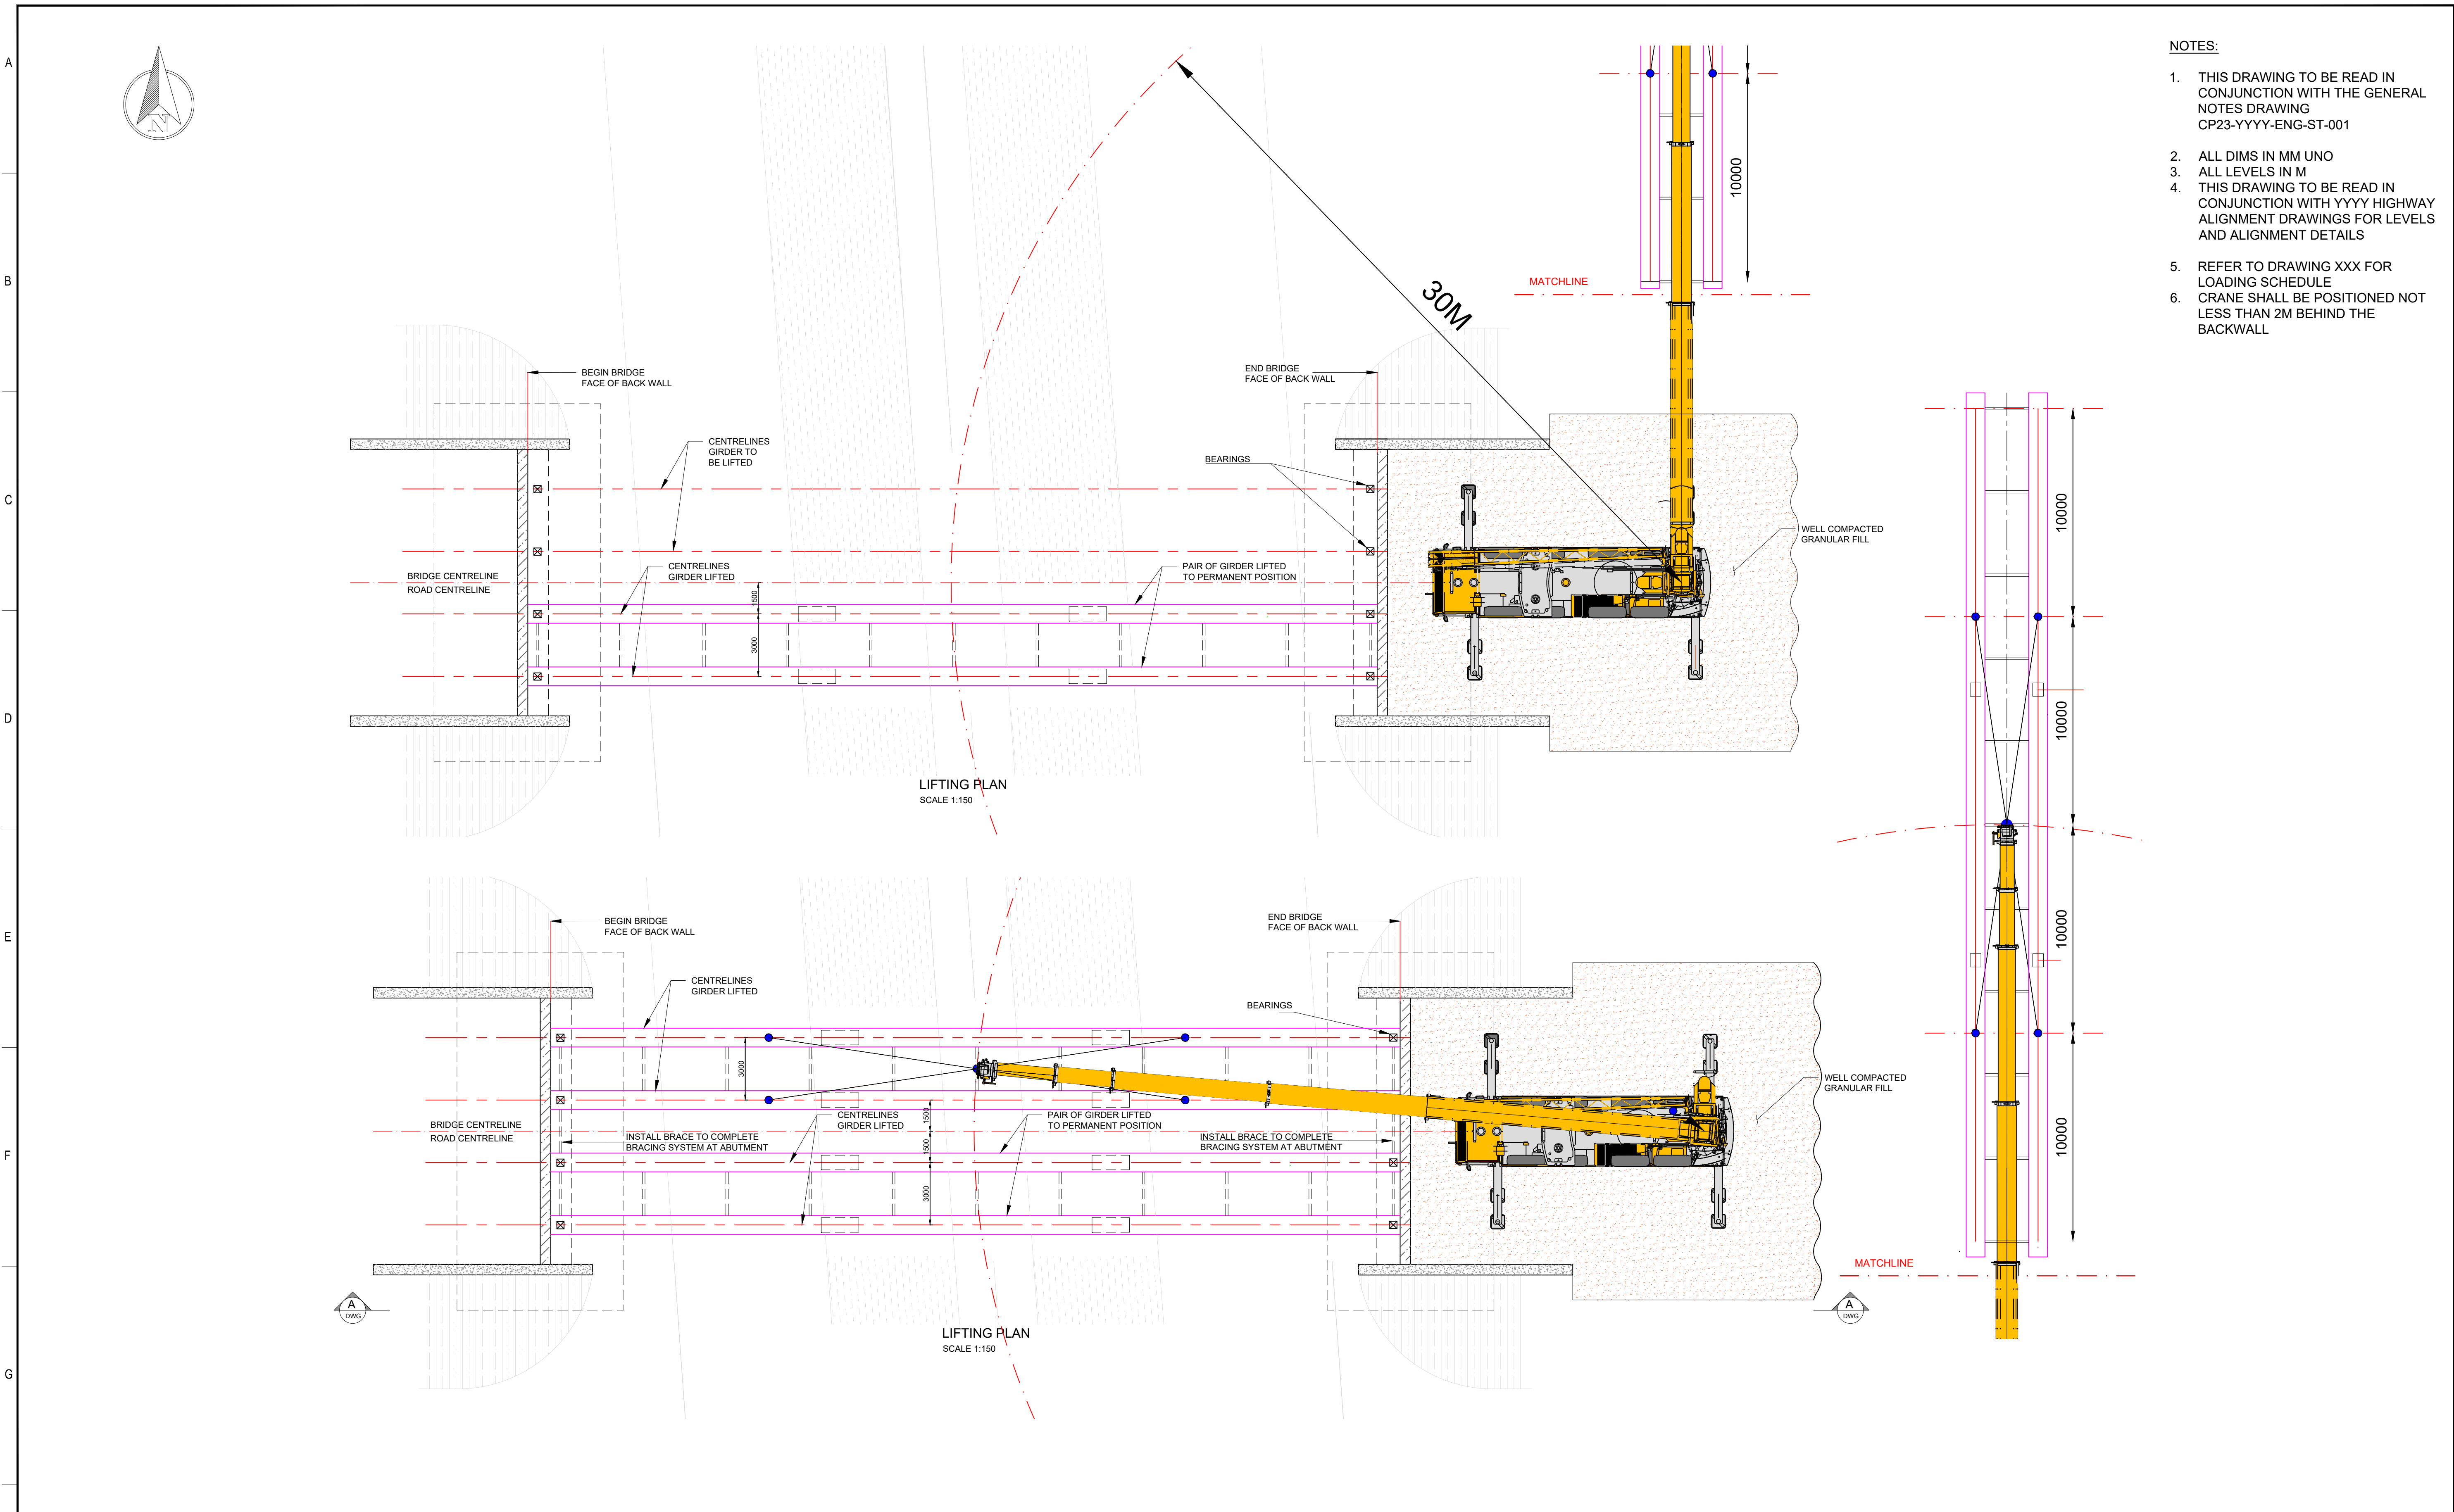

- NOTES:
1. THIS DRAWING TO BE READ IN CONJUNCTION WITH THE GENERAL NOTES DRAWING CP23-YYYY-ENG-ST-001
 2. ALL DIMS IN MM UNO
 3. ALL LEVELS IN M
 4. THIS DRAWING TO BE READ IN CONJUNCTION WITH YYYY HIGHWAY ALIGNMENT DRAWINGS FOR LEVELS AND ALIGNMENT DETAILS
 5. REFER TO DRAWING XXX FOR LOADING SCHEDULE
 6. CRANE SHALL BE POSITIONED NOT LESS THAN 2M BEHIND THE BACKWALL

1). THIS DRAWING IS TO BE READ IN CONJUNCTION WITH ALL OTHER RELEVANT DRAWINGS, ANY DISCREPANCIES, ERRORS OR OMISSIONS TO BE BROUGHT TO THE ATTENTION OF CPLEX COMPANY LTD-ENG DIV. 2). ALL DIMENSIONS TO BE CHECKED BEFORE COMMENCEMENT OF WORK ON SITE.						KEY TO HEALTH & SAFETY SYMBOLS:  WARNING RISK: INDICATES A RESIDUAL RISK AS A WARNING  COMPULSORY RISK: INDICATES A RESIDUAL RISK REQUIRING A COMPULSORY ACTION  PROHIBITIVE RISK: INDICATES A RESIDUAL RISK REQUIRING A PROHIBITIVE ACTION  INFORMATION RISK: INDICATES A RESIDUAL RISK FOR INFORMATION		 GOVERNMENT OF THE REPUBLIC OF GHANA MINISTRY OF ROADS AND HIGHWAYS GHANA HIGHWAY AUTHORITY		Project: SINGLE SPAN 40M STEEL BRIDGE		Purpose of issue: PRELIMINARY		Status:	
	Client Project Number:		Scale: AS SHOWN		Drawing Sheet Size: A1										
	Drawing: LIFTING OF STEEL GIRDERS		DO NOT SCALE FROM THIS DRAWING		Sheet Number: 1 of 1										
	Drawing Number: CPLX-ENG-ST-DW-008		Rev.: P01												
P01 IS WKK	DISCUSSION	01/02/25	ST												
REV. DRN. CKD.	COMMENTS	DATE	APD.												