
NOTES:

1. THIS DRAWING TO BE READ IN CONJUNCTION WITH THE GENERAL NOTES DRAWING CP23-YYYY-ENG-ST-001
2. ALL DIMS IN MM UNO
3. ALL LEVELS IN M
4. THIS DRAWING TO BE READ IN CONJUNCTION WITH YYYY HIGHWAY ALIGNMENT DRAWINGS FOR LEVELS AND ALIGNMENT DETAILS
5. BOREHOLE LOCATION IS INDICATIVE
6. FOR BEARING AND AND EXPANSION JOINT DETAILS REFER TO DWG ZZZZ

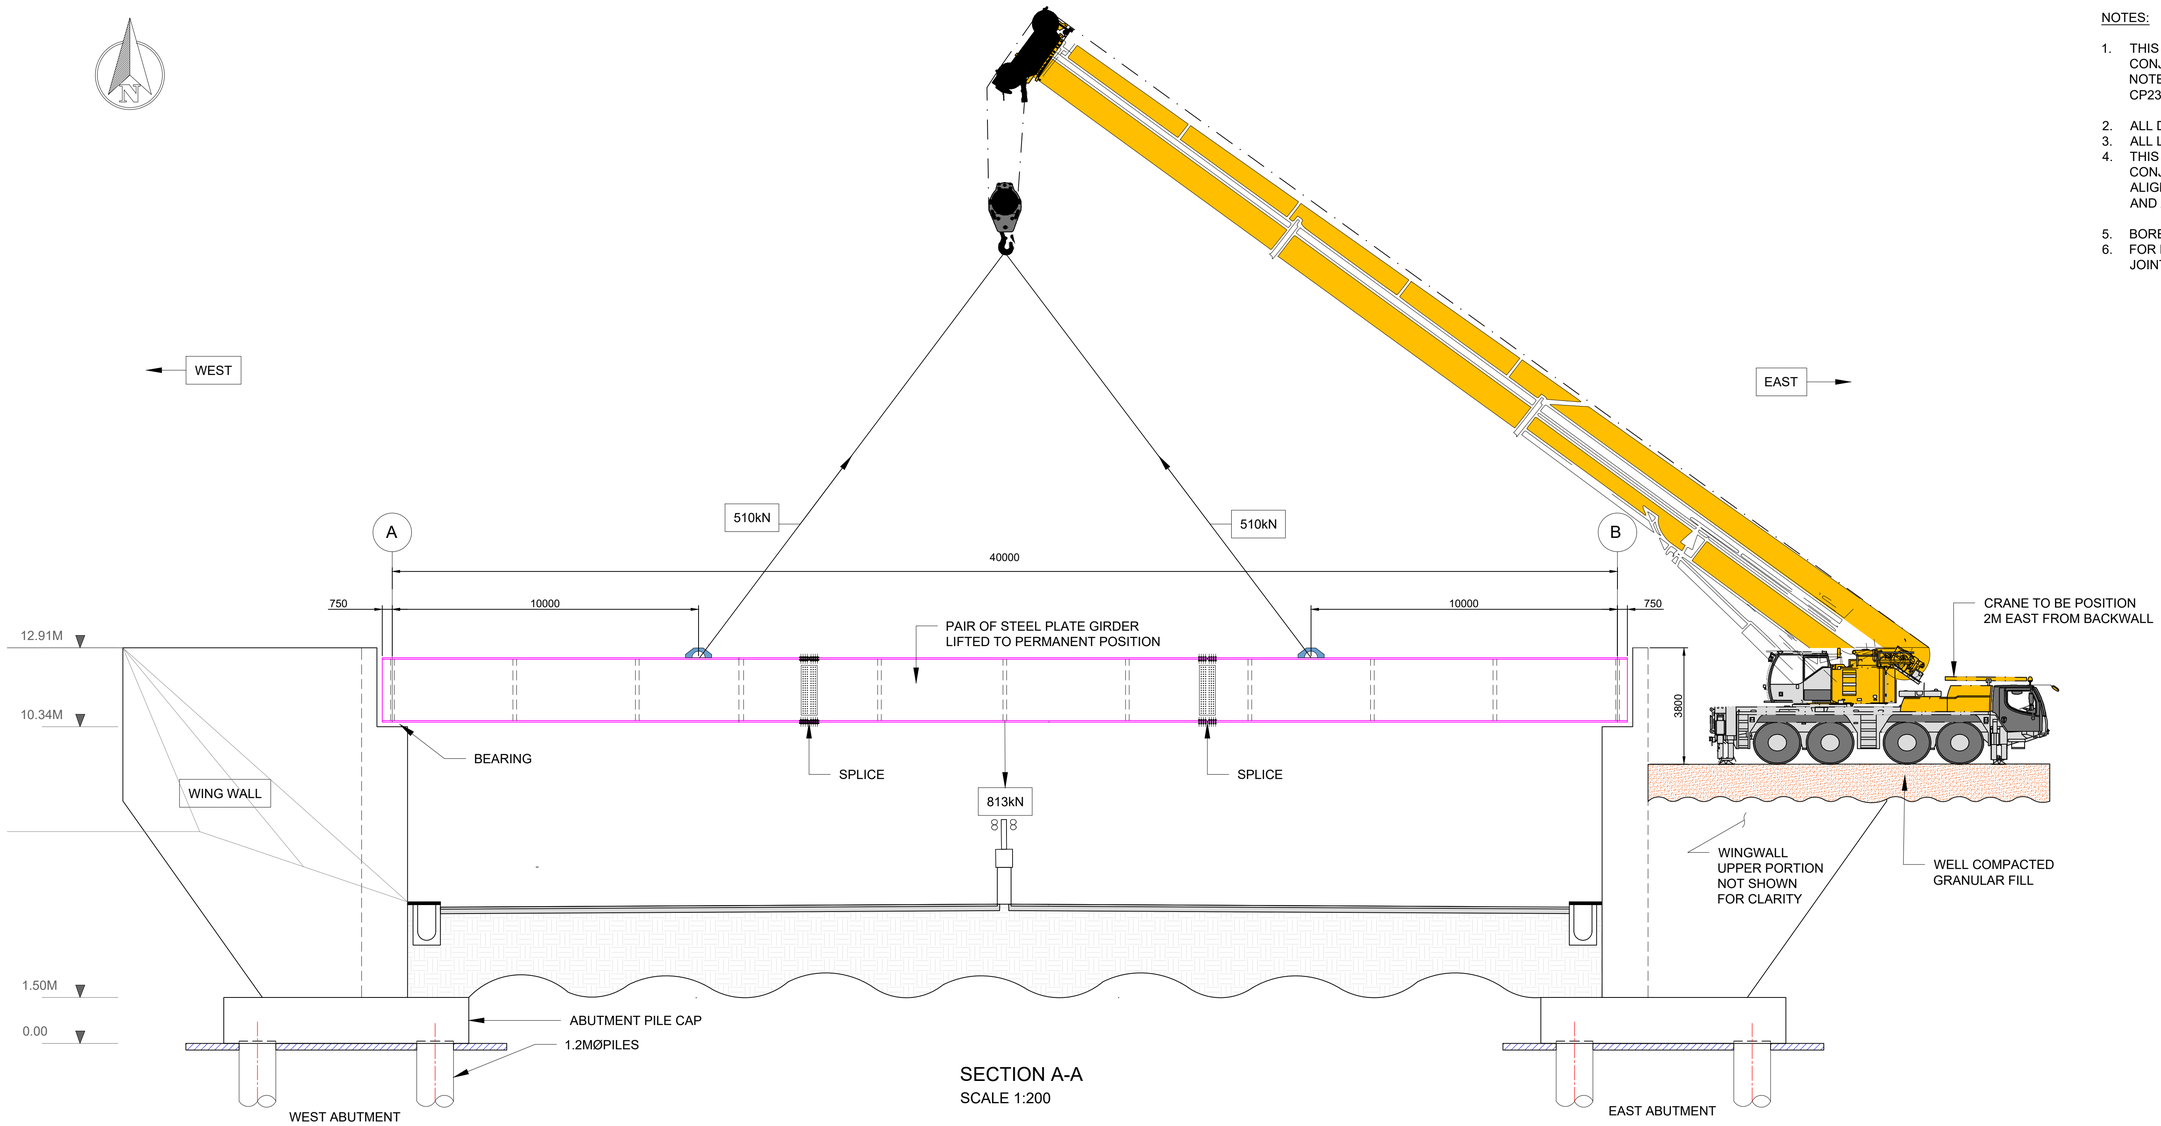

SECTION A-A
SCALE 1:200

1). THIS DRAWING IS TO BE READ IN CONJUNCTION WITH ALL OTHER RELEVANT DRAWINGS, ANY DISCREPANCIES, ERRORS OR OMISSIONS TO BE BROUGHT TO THE ATTENTION OF CPLEX COMPANY LTD-ENG DIV.
2). ALL DIMENSIONS TO BE CHECKED BEFORE COMMENCEMENT OF WORK ON SITE.

REV.	DRN.	CKD.	COMMENTS	DATE	APD.
P01	IS	WGK	DISCUSSION	01/02/25	ST

KEY TO HEALTH & SAFETY SYMBOLS:

- WARNING RISK: INDICATES A RESIDUAL RISK AS A WARNING
- COMPULSORY RISK: INDICATES A RESIDUAL RISK REQUIRING A COMPULSORY ACTION
- PROHIBITIVE RISK: INDICATES A RESIDUAL RISK REQUIRING A PROHIBITIVE ACTION
- INFORMATION RISK: INDICATES A RESIDUAL RISK FOR INFORMATION

CPLEX Company Ltd
ENGINEERS & CONTRACTORS

GOVERNMENT OF THE REPUBLIC OF GHANA
MINISTRY OF ROADS AND HIGHWAYS
GHANA HIGHWAY AUTHORITY

Project: SINGLE SPAN 40M STEEL BRIDGE

Drawing: LIFTING OF STEEL GIRDGERS ELEVATION

Purpose of issue: PRELIMINARY	Status:	
Client Project Number:	Scale: AS SHOWN	Drawing Sheet Size: A1
DO NOT SCALE FROM THIS DRAWING		Sheet Number: 1 of 1
Drawing Number: CPLX-ENG-ST-DW-009		Rev.: P01